


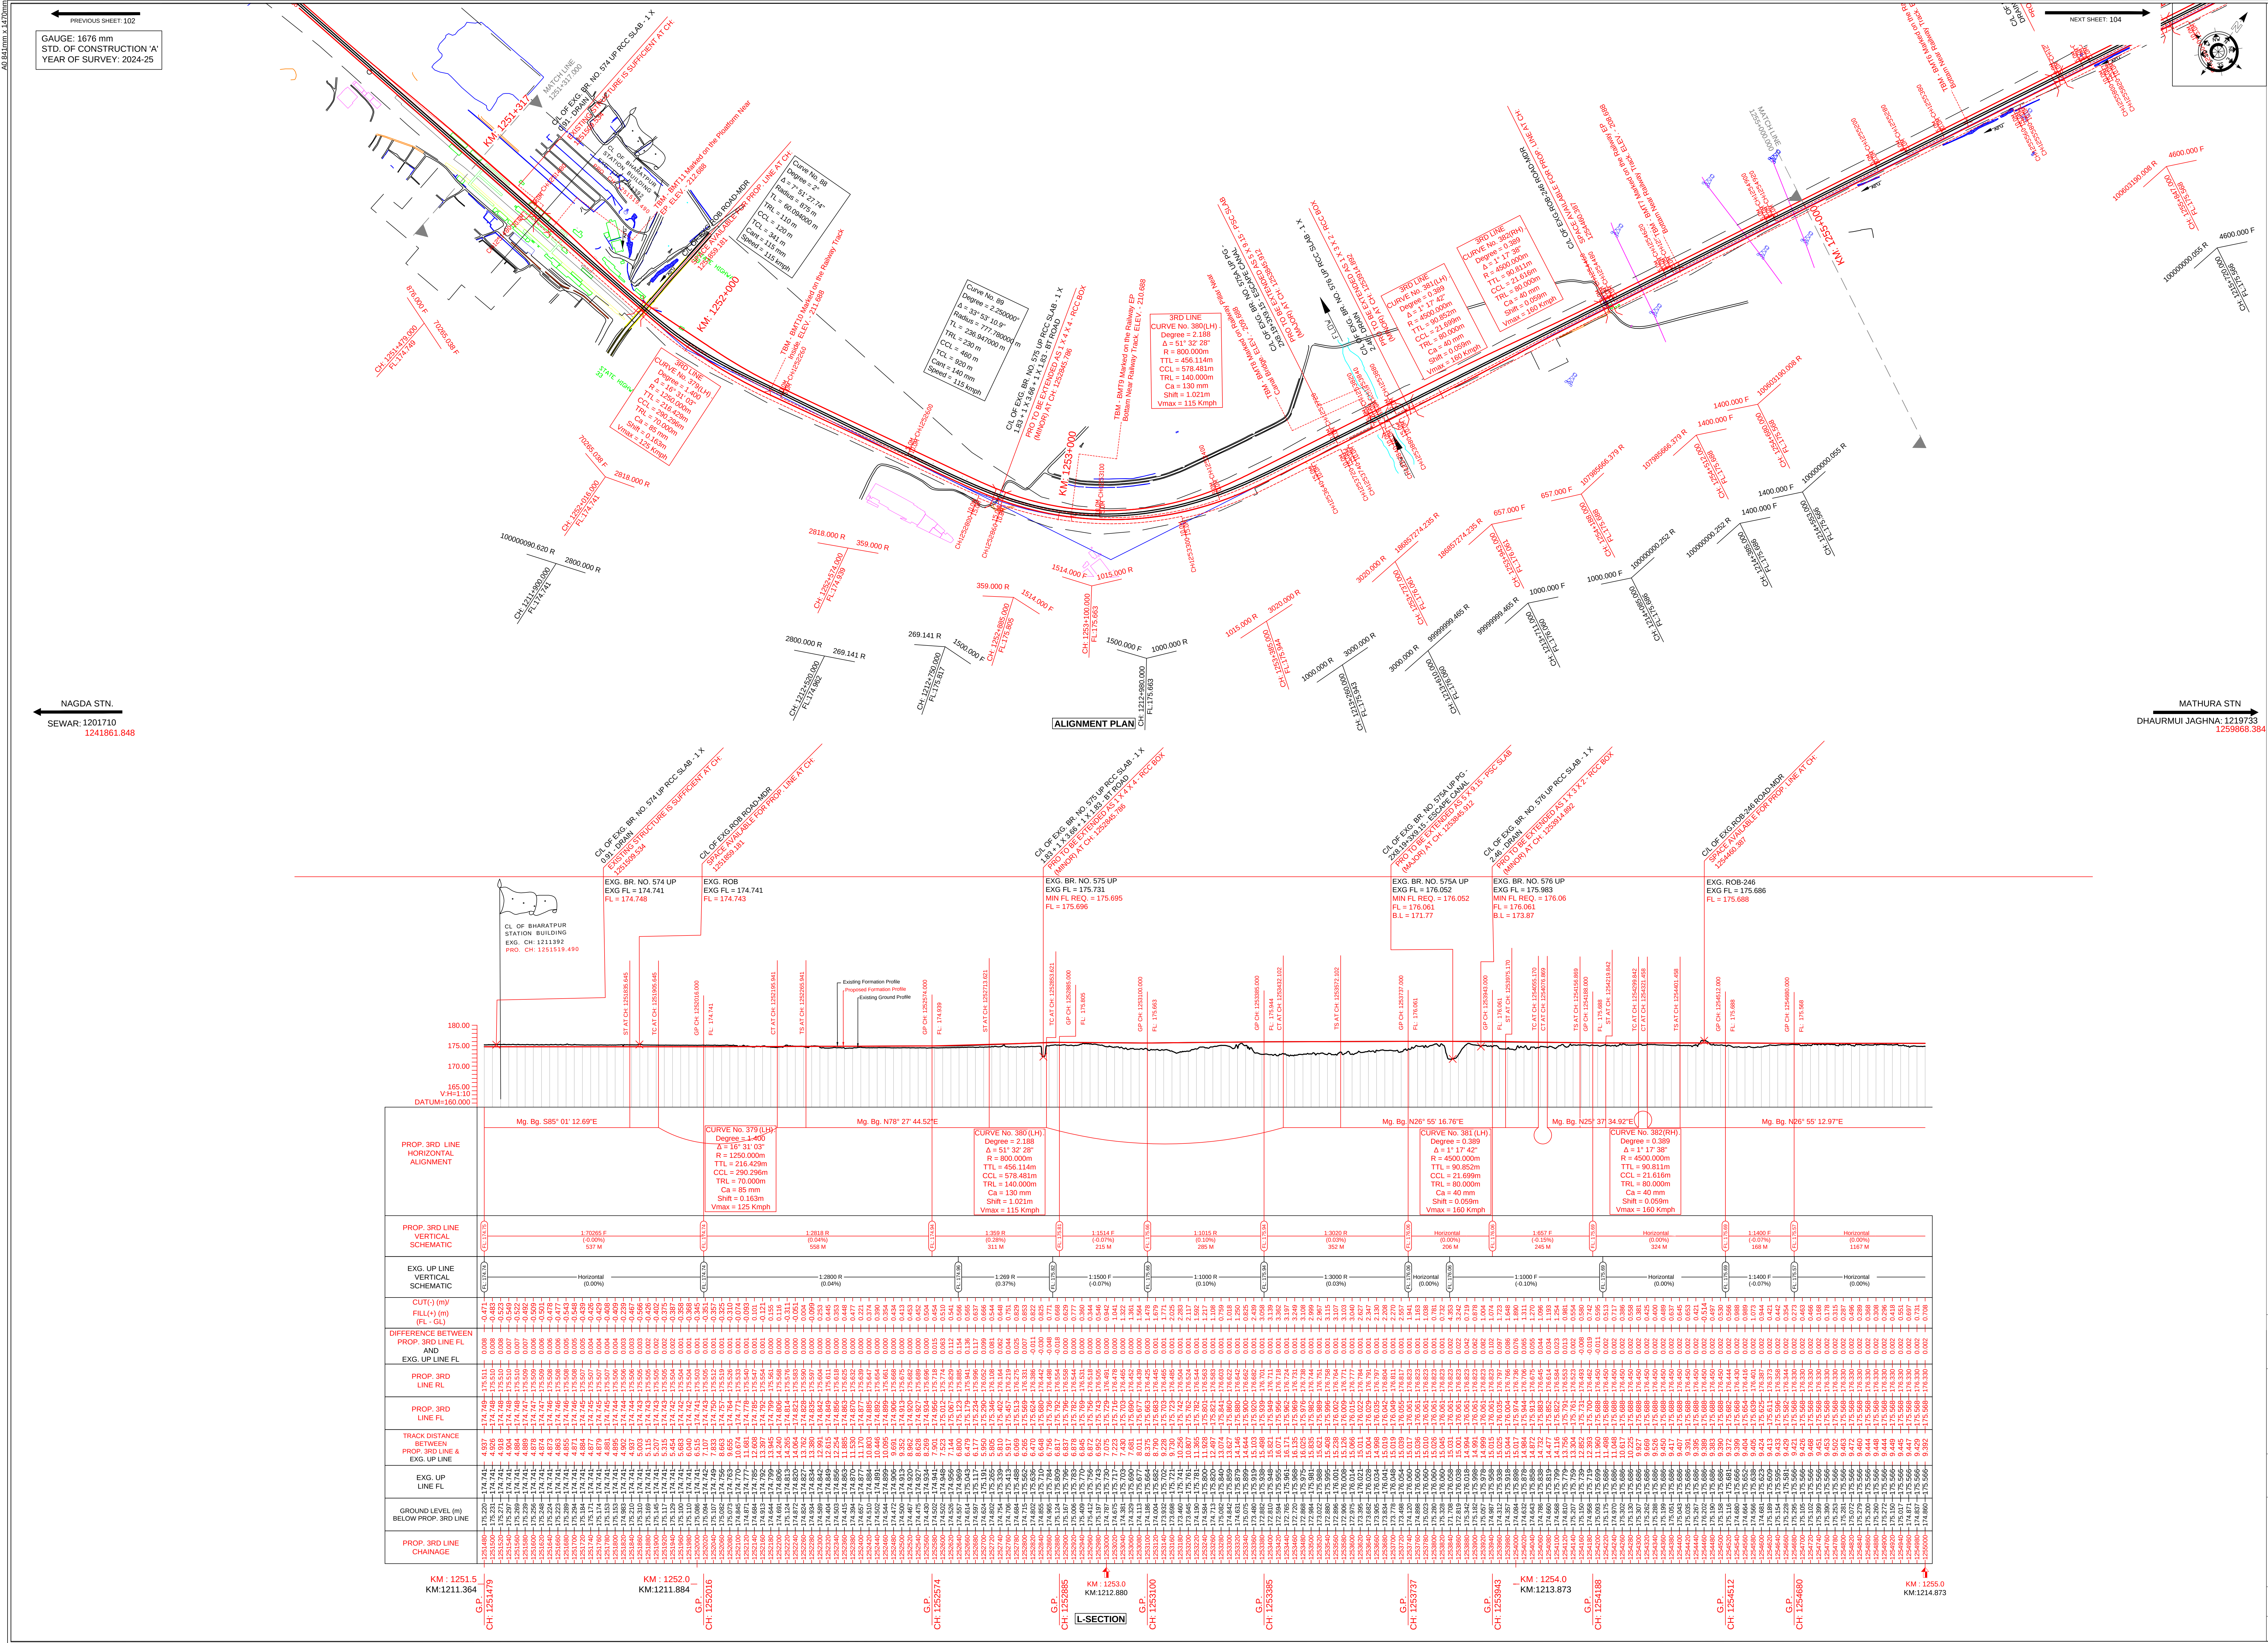

NOTE:

- ALL DIMENSIONS ARE IN METERS, UNLESS OTHERWISE SPECIFIED.
- EXISTING WORK SHOWN IN BLACK.
- PROPOSED WORK SHOWN IN RED.
- AS PER TERMS OF REFERENCE YARD GRADIENT HAVE BEEN EASED TO THE EXTENT POSSIBLE MAINTAINING GRADIENT AS 1 IN 150 (COMPENSATED).
- RAIL LEVEL SHOULD BE 762 MM ABOVE FORMATION LEVEL FOR TRACK STRUCTURE OF 60 KG NEW RAIL ON PSC WIDER SLEEPER (1660 NOS PER KM) WITH 350 MM BALLAST CUSHION.
- RULING GRADIENT OF THIS SECTION IS 1 IN 150.
- AS PER ENGINEERING CODE, VERTICAL CURVE WILL BE PROVIDED AT SITE WHERE ALGEBRAIC DIFFERENCE BETWEEN TWO GRADES IS EQUAL OR MORE THAN 4MM PER METER OR 0.4%.
- LAND TO BE ACQUIRED SHOWN IN DASHED RED.
- THE CHAINAGE AND KILOMETERS SHOWN ARE RECKONED FROM CENTER LINE OF STATION BUILDING AS 0.00
- THE SECTION IS DESIGNED FOR MAXIMUM SECTIONAL SPEED OF 160 KMPH.
- THE PROPOSED FORMATION AND BRIDGES IN THE SECTION IS DESIGNED FOR 25 T-2008 AXLE LOADING.

TBM DETAILS

TBM ID	Chainage	Easting	Northing	MSL	Description
BMT11	1251559.832	746417.145	3015112.625	212.688	Marked on the Platform Near EP.
BMT10	1252229.156	747082.437	3015121.108	211.688	Marked on the Railway Track Inside
BMT9	1253030.121	747856.372	3015311.629	210.688	Marked on the Railway EP Bottom Near Railway Track
BMT8	1253814.768	748309.348	3015930.151	209.688	Marked on Railway Pillar Near Canal Bridge.
BMT7	1254658.599	748691.515	3016682.422	208.688	Marked on the Railway EP Bottom Near Railway Track

LEGENDS:

EXISTING RAILWAY TRACK:

EXISTING ROW:

PROPOSED RAILWAY TRACK:

PROPOSED ROW:

PRO. BRIDGES:

ELECTRIC LINES:

HT LINES:

WATER BODIES:

RAILWAY STRUCTURES:

EXISTING ROW:

METAL ROAD:

UN-METAL ROAD:

ABBREVIATIONS

Δ = Radius PVI = Point of Vertical Intersection L = Length

$\triangle$ = Angle TTP1 = Tangent to Transition Point-1 FL = Formation Level

TRL = Transition Length CTP1 = Curve Tangent Point-1 RL = Rail Level

TL = Tangent Length CTP2 = Curve Tangent Point-2 G = Gradient

SL = Straight Line Length TTP2 = Tangent to Transition Point-2

CL = Curve Length BVC = Beginning of Vertical Curve

CCL = Circular Curve Length EVC = End of Vertical Curve

IP = Intersection Point ERL = Existing Rail Level

RTL = Road Top Level BL = Bed Level

ISSUE RECORD

No.	DATE	REV	PREPARED BY	CHECKED BY	APPROVED BY
1	01-07-2025	R0	SIVA THUTA	RAMMOHAN	RAMAKRISHNA

CLIENT: WEST CENTRAL RAILWAY KOTA DIVISION

PROJECT : CONDUCTING FINAL LOCATION SURVEY (FLS) INCLUDING PREPARATION OF DPR, GEOTECHNICAL INVESTIGATION, SIGNALING WORK, ELECTRICAL WORKS AND OPERATING/TRAFFIC WORK FOR CONSTRUCTION OF ELECTRIFIED NEW LINE/DOUBLING/THIRD LINE/4TH LINE. FLY OVER WORK/BYPASS LINE ETC.

TITLE : DETAILED PLAN AND L SECTION MATHURA-NAGDA -3RD LINE 1251+480.000 TO 1255+000.000


CONSULTANT: aarvee engineering consultants limited.

DRG.No: AA/WCR/FLS/2616/MKN-3RD/P&P/103

SCALE : HOR : 1:5000, VER : 1:500

SHEET NO : 103

DATE : 01-07-2025

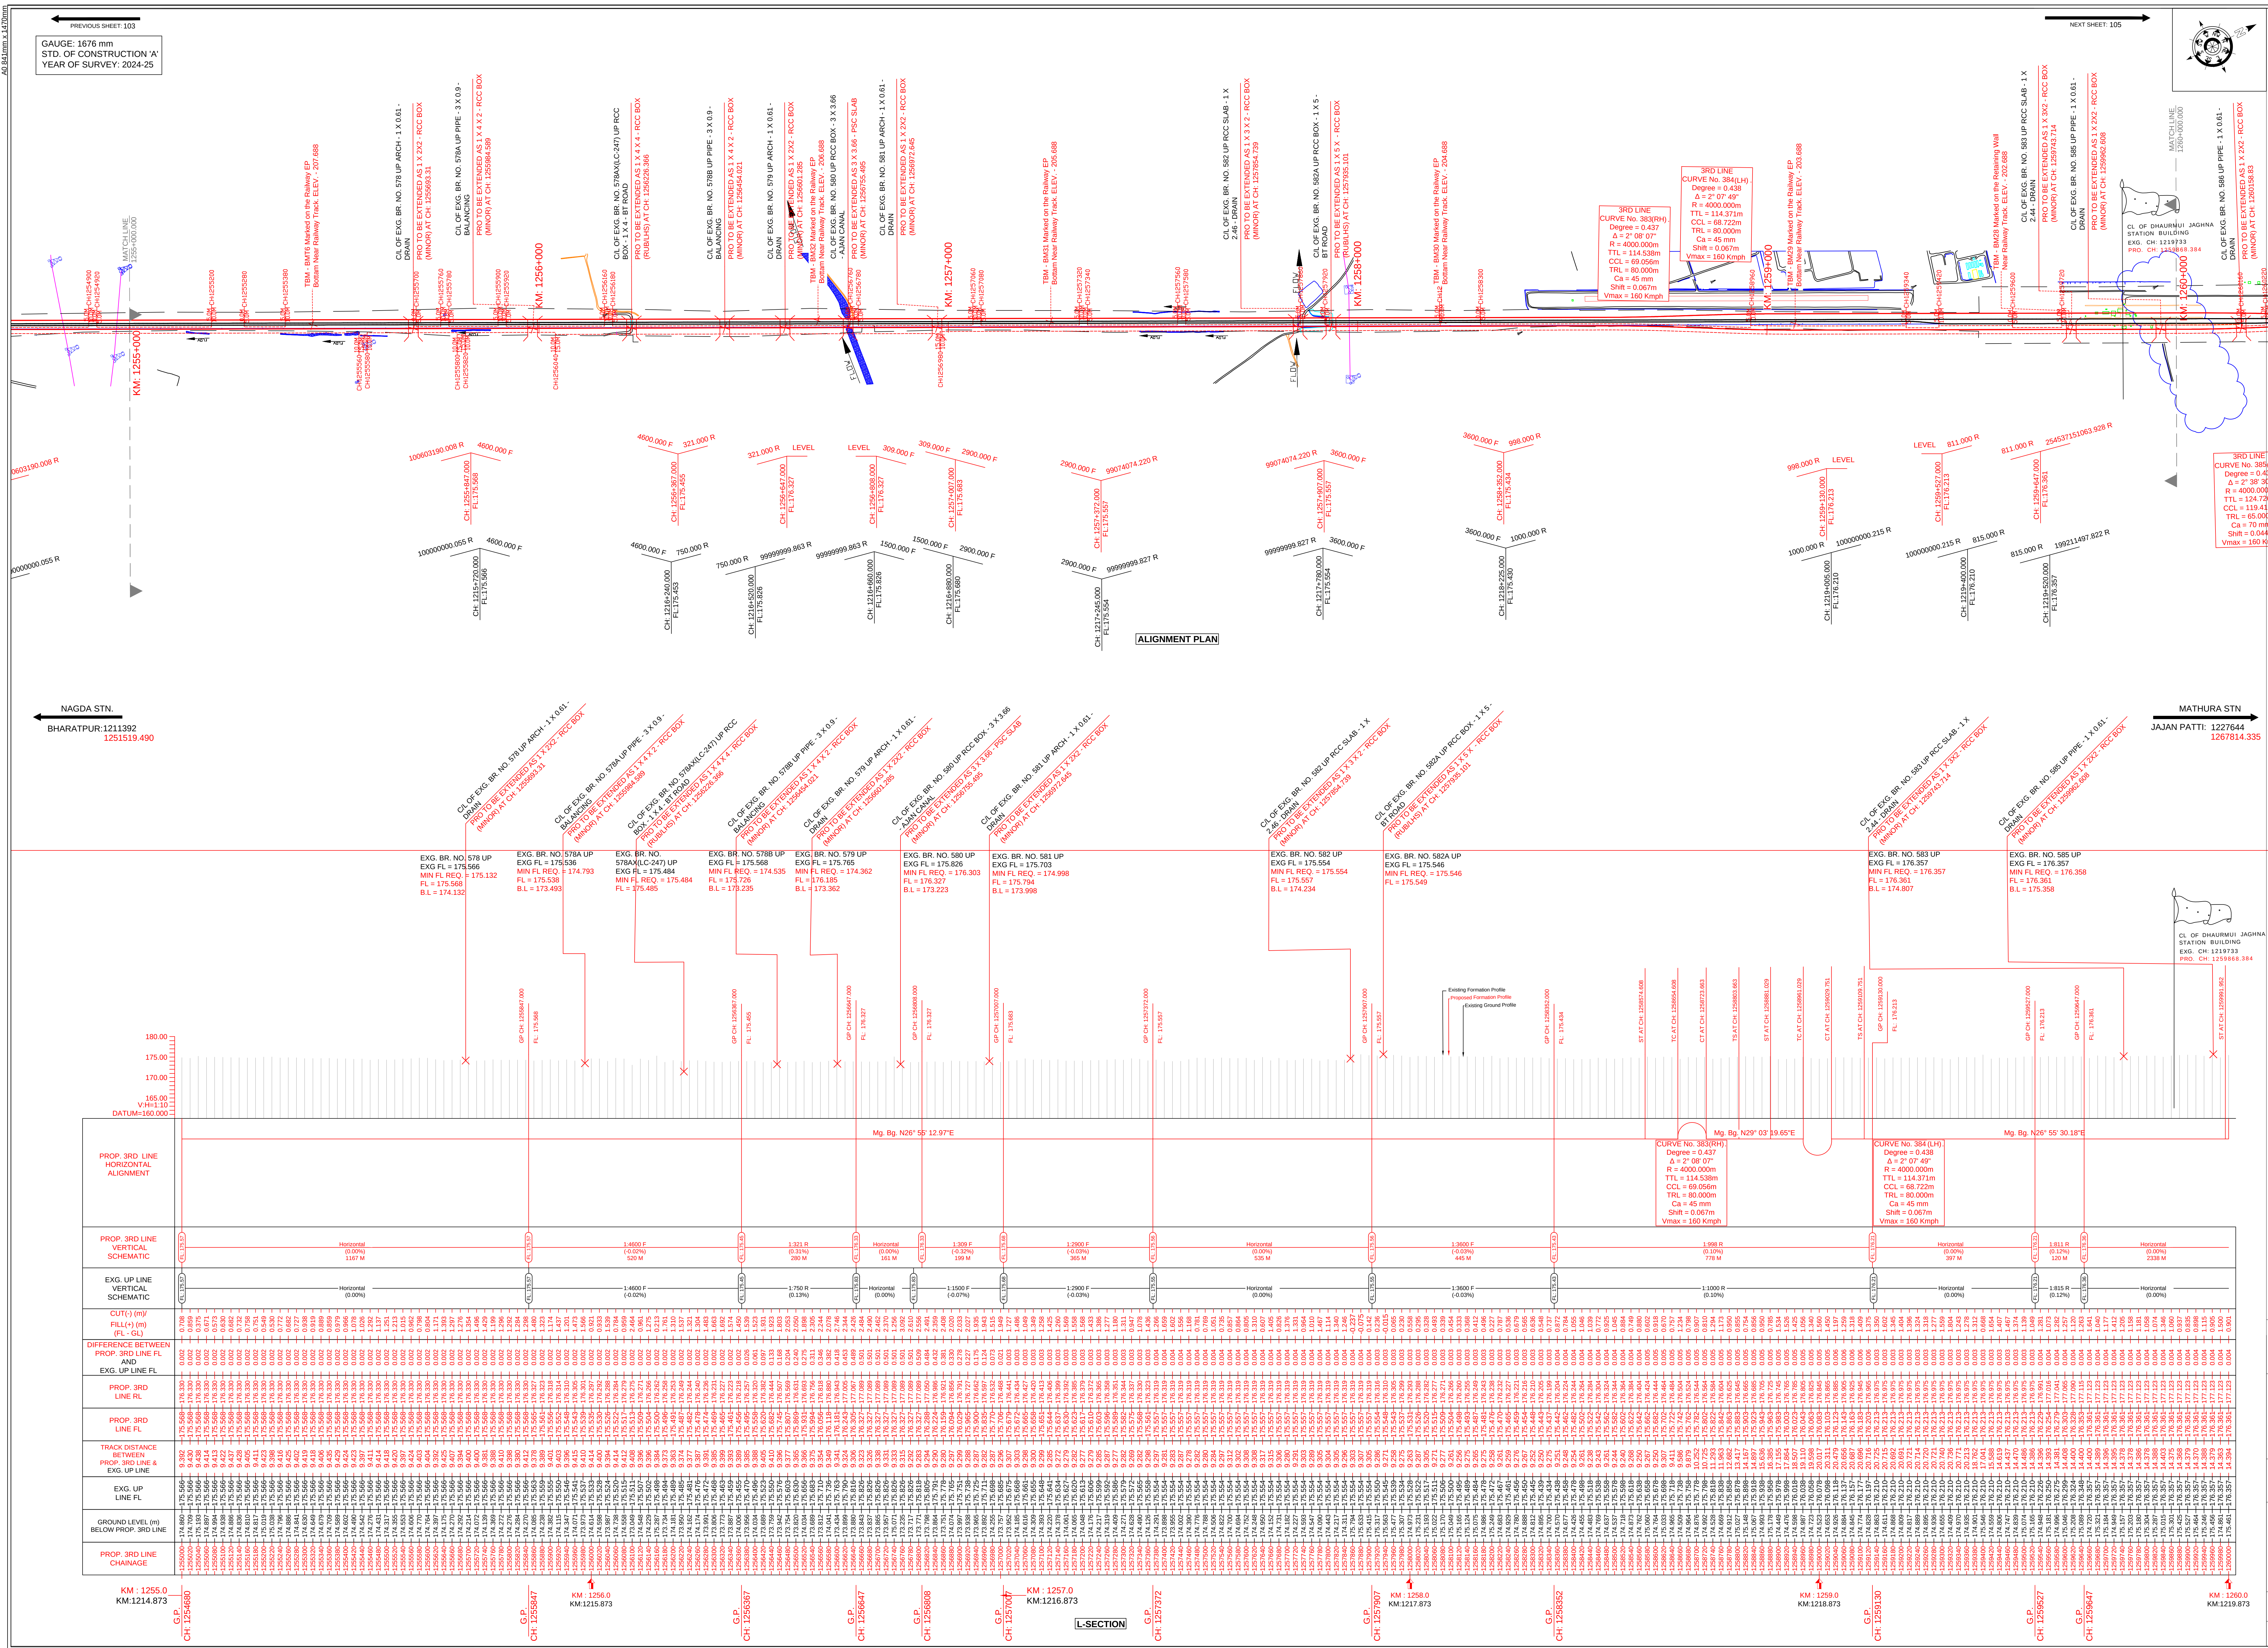

- NOTE:
1. ALL DIMENSIONS ARE IN METERS, UNLESS OTHERWISE SPECIFIED.
 2. EXISTING WORK SHOWN IN BLACK.
 3. PROPOSED WORK SHOWN IN RED.
 4. AS PER TERMS OF REFERENCE YARD GRADIENT HAD BEEN EASED TO THE EXTENT POSSIBLE MAINTAINING GRADIENT AS 1 IN 150 (COMPENSATED).
 5. RAIL LEVEL SHOULD BE 762 MM ABOVE FORMATION LEVEL FOR TRACK STRUCTURE OF 60 KG NEW RAIL ON PSC WIDER SLEEPER (1660 NCS PER KM) WITH 100 MM BALLAST CUSHION.
 6. RULING GRADIENT OF THIS SECTION IS 1 IN 150.
 7. AS PER ENGINEERING CODE, VERTICAL CURVE WILL BE PROVIDED AT SITE WHERE ALGEBRAIC DIFFERENCE BETWEEN TWO GRADES IS EQUAL OR MORE THAN 4MM PER METER OR 0.4%.
 8. LAND TO BE ACQUIRED SHOWN IN DASHED RED.
 9. THE CHAINAGE AND KILOMETERS DISTANCES ARE RECKONED FROM CENTER LINE OF STATION BUILDING AS 0.00.
 10. THE SECTION IS DESIGNED FOR MAXIMUM SECTIONAL SPEED OF 160 KMPH.
 11. THE PROPOSED FORMATION AND BRIDGES IN THE SECTION IS DESIGNED FOR 25 T-2008 AXLE LOADING.

TBM DETAILS					
TBM ID	Chainage	Easting	Northing	MSL	Description
BM76	1255446.571	749047.074	3017365.614	207.688	Marked on the Railway EP Potam Near Railway Track
BM32	1256681.757	749599.984	3018490.161	206.688	Marked on the Railway EP Potam Near Railway Track
BM31	1257250.401	749861.052	3018995.35	205.688	Marked on the Railway EP Potam Near Railway Track
BM30	1258204.305	750294.739	3019844.97	204.688	Marked on the Railway EP Potam Near Railway Track
BM29	1259068.885	750692.081	3020612.716	203.688	Marked on the Railway EP Potam Near Railway Track
BM28	1259738.459	750996.872	3021208.954	202.688	Marked on the Reservoir Wall Near Railway Track.

LEGENDS:

EXISTING RAILWAY TRACK		EXISTING ROAD	
"PROPOSED RAILWAY TRACK		METAL ROAD	
"PROPOSED ROW		UN-METAL ROAD	
"PRO. BRIDGES			
"ELECTRIC LINES			
HT LINES			
"WATER BODIES			
"RAILWAY STRUCTURES			

ABBREVIATIONS

R	= Radius	PVI	= Point of Vertical Intersection	L	= Length
Δ	= Angle	PTP1	= Tangent to Transition Point-1	L _F	= Formation Level
TRL	= Transition Length	CTP1	= Curve Tangent Point-1	RL	= Rail Level
TL	= Tangent Length	CTP2	= Curve Tangent Point-2	G	= Gradient
SL	= Straight Line Length	PTP2	= Tangent to Transition Point-2		
CL	= Curve Length	BVC	= Beginning of Vertical Curve		
CCL	= Circular Curve Length	EVC	= End of Vertical Curve		
IP	= Intersection Point	ERL	= Existing Rail Level		
RTL	= Road Top Level	BL	= Bed Level		

REFERENCE DRAWINGS	
DRAWING TITLE	DRAWING No.
DRG.NO.DY.CE(C)KOTA	
H.Q. DRG. NO.- CPM/KOTA/E	
NAME OF THE OFFICER & DESIGNATION	SIGNATURE
(VIJAY PANDEY) CPM/WCR/KOTA	
(GAURAV MISHRA) DY.CE/C/KOTA	
(RAJESH YADAV) AXEN/KOTA	
(P.K. KANWA) SSE/W/C/KOTA	
(L.S. MEENA) JE/DRG/KOTA	

ISSUE RECORD					
1	01-07-2025	R0	SIVA THUTA	RAMMOHAN	RAMAKRISHNA
No.	DATE	REV	PREPARED BY	CHECKED BY	APPROVED BY

CLIENT:

WEST CENTRAL RAILWAY
KOTA DIVISION

PROJECT: CONDUCTING FINAL LOCATION SURVEY (FLS) INCLUDING PREPARATION OF DPR, GEOTECHNICAL INVESTIGATION, SIGNALING WORK, ELECTRICAL WORKS AND OPERATING/TRAFFIC WORK FOR CONSTRUCTION OF ELECTRIFIED NEW LINE/DOUBLING/THIRD LINE/4TH LINE. FLY OVER WORK/BYPASS LINE ETC.

1255+000.000 TO 1260+000.000


CONSULTANT :



DRG.No: AA/WCR/FLS/2616/MKN-3RD/P&P/104

SHEET NO : 104

DATE : 01-07-2025

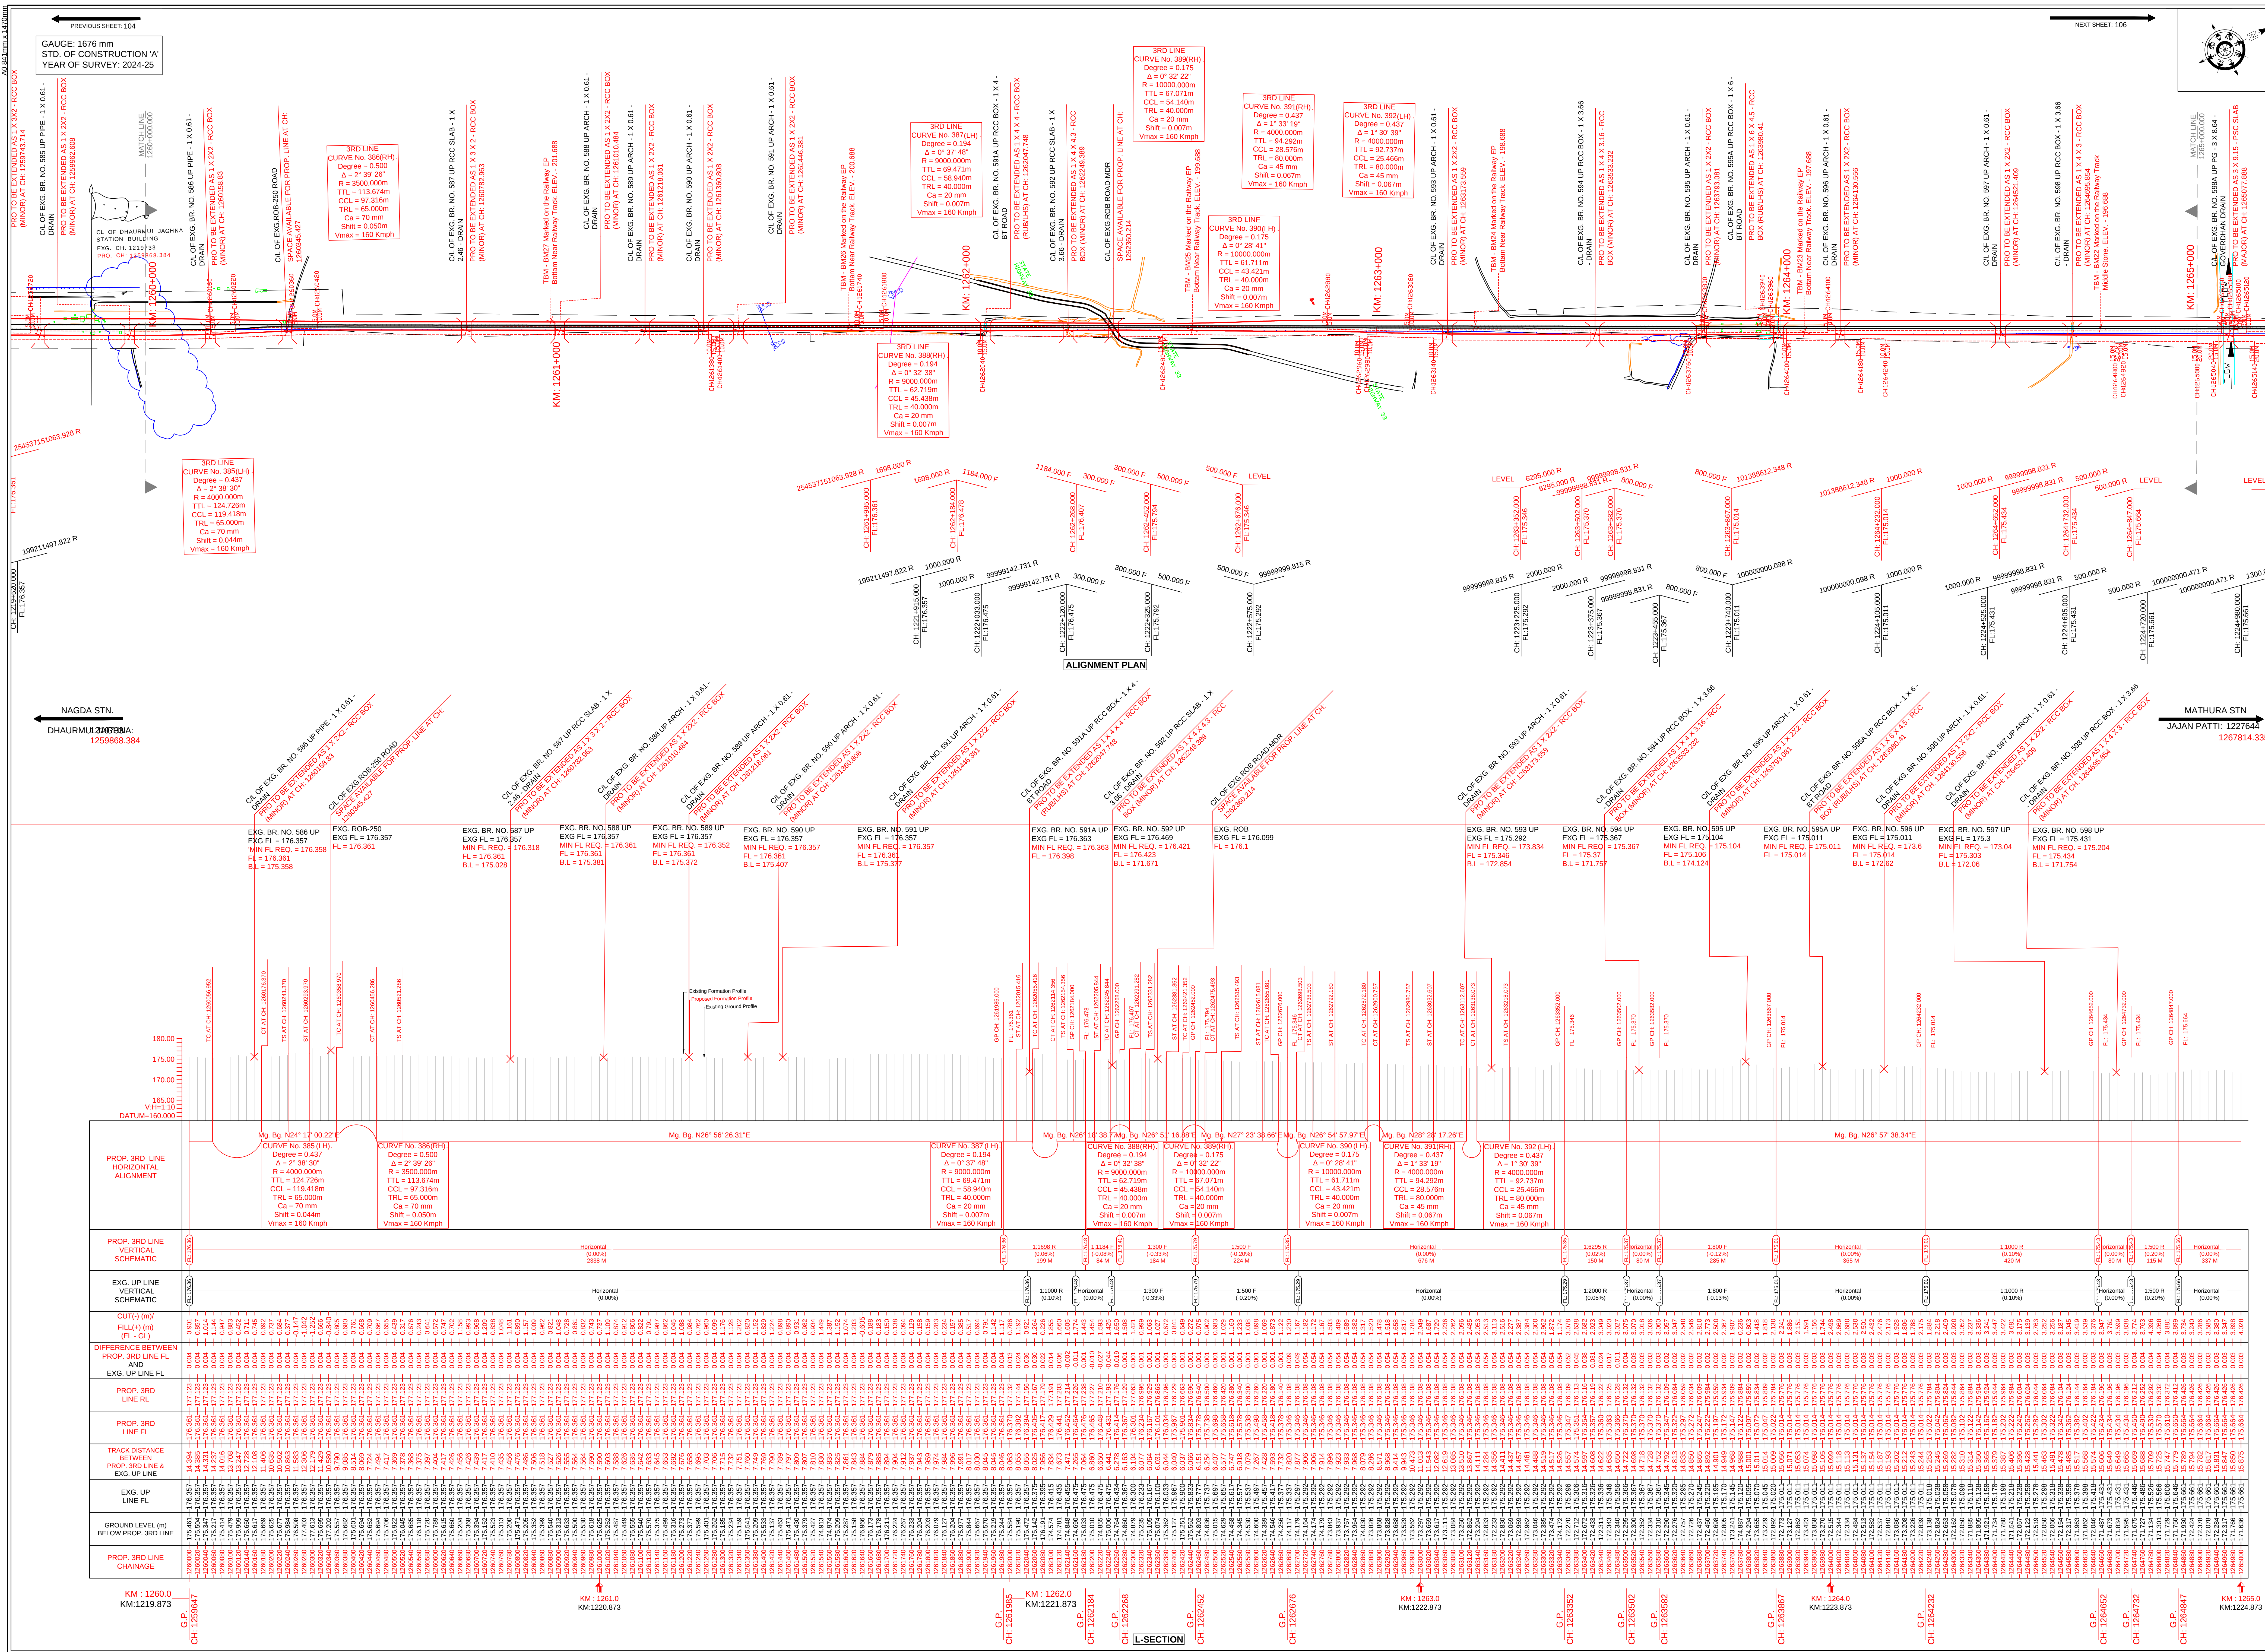

- NOTE:
1. ALL DIMENSIONS ARE IN METERS, UNLESS OTHERWISE SPECIFIED
 2. EXISTING WORK SHOWN IN BLACK
 3. PROPOSED WORK SHOWN IN RED.
 4. AS PER TERMS OF REFERENCE YARD GRADIENT HAVE BEEN EASED TO THE EXTENT POSSIBLE MAINTAINING GRADIENT AS 1 IN 10 (COMPENSATED).
 5. RAIL LEVEL SHOULD BE 762 MM ABOVE FORMATION LEVEL FOR TRACK STRUCTURE OF 76 KG NEW RAIL ON PSC WIDER SLEEPER (1560 NOS PER KM) WITH 35% BALLAST CUSHION.
 6. RULING GRADIENT OF THIS SECTION IS 1 IN 150.
 7. AS PER ENGINEERING CODE, VERTICAL CURVE WILL BE PERFORMED AT SITE WHERE ALGEBRAIC DIFFERENCE BETWEEN TWO GRADES IS EQUAL OR MORE THAN 4MM PER METER OR 0.4%.
 8. LAND TO BE ACQUIRED SHOWN IN DASHED RED.
 9. THE CHAINAGE AND KILOMETERS SHOWN ARE RECKONED FROM CENTER LINE OF TRACK AND ARE AS 0.00.
 10. THE SECTION IS DESIGNED FOR MAXIMUM SECTIONAL SPEED OF 160 KMPH.
 11. THE PROPOSED FORMATION AND BRIDGES IN THE SECTION IS DESIGNED FOR 25 T-2008 AXLE LOADING.

TBM DETAILS					
TBM ID	Chainage	Easting	Northing	MSL	Description
BM27	1260988.735	751544.558	3022332.713	201.688	Marked on the Railway EF Bottom Near Railway Track
BM26	1261713.119	751886.82	3022971.335	200.688	Marked on the Railway EF Bottom Near Railway Track
BM25	1262551.727	752268.831	3023717.886	199.688	Marked on the Railway EF Bottom Near Railway Track
BM24	1263240.102	752572.219	3024335.783	198.688	Marked on the Railway EF Bottom Near Railway Track
BM23	1264044.343	752947.932	3025046.978	197.688	Marked on the Railway EF Bottom Near Railway Track
BM22	1264765.365	753264.094	3025695.098	196.688	Marked on the Railway Track Middle Stone

LEGENDS:

EXISTING RAILWAY TRACK		EXISTING ROW	
PROPOSED RAILWAY TRACK		METAL ROAD	
PROPOSED ROW		UN-METAL ROAD	
PRO. BRIDGES			
ELECTRIC LINES			
HT LINES			
WATER BODIES			
RAILWAY STRUCTURES			

ABBREVIATIONS

R = Radius	PVI = Point of Vertical Intersection	L = Length
Δ = Angle	PTP1 = Tangent to Transition Point-1	FL = Formation Level
TRL = Transition Length	CTP1 = Curve Tangent Point-1	RL = Rail Level
TL = Tangent Length	CTP2 = Curve Tangent Point-2	G = Gradient
SL = Straight Line Length	PTP2 = Tangent to Transition Point-2	
CL = Curve Length	BVC = Beginning of Vertical Curve	
CCL = Circular Curve Length	EVC = End of Vertical Curve	
IP = Intersection Point	ERL = Existing Rail Level	
RTL = Road Top Level	BL = Bed Level	

REFERENCE DRAWINGS

DRAWING TITLE	DRAWING No.
DRG NO.DY.CE/CJKOTA	
H.Q. DRG. NO.- CPMKOTA/E	
NAME OF THE OFFICER & DESIGNATION	SIGNATURE
(VIJAY PANDEY) CPM/WCR/KOTA	
(GAURAV MISHRA) DY.CE/CJKOTA	
(RAJESH YADAV) AXEN/KOTA	
(P.K. KANWA) SSE/W/CJKOTA	
(L.S. MEENA) JE/DRG/KOTA	

ISSUE RECORD					
1	01-07-2025	R0	SIVA THUTA	RAMMOHAN	RAMAKRISHNA
No.	DATE	REV	PREPARED BY	CHECKED BY	APPROVED BY

CLIENT:

WEST CENTRAL RAILWAY
KOTA DIVISION


PROJECT: CONDUCTING FINAL LOCATION SURVEY (FLS) INCLUDING PREPARATION OF DPR, GEOTECHNICAL INVESTIGATION, SIGNALING WORK, ELECTRICAL WORKS AND OPERATING/TRAFFIC WORK FOR CONSTRUCTION OF ELECTRIFIED NEW LINE/DOUBLING/THIRD LINE/4TH LINE. FLY OVER WORK/BYPASS LINE ETC.

TITLE : DETAILED PLAN AND L SECTION MATHURA-NAGDA -3RD LINE
1260+000.000 TO 1265+000.000

CONSULTANT :

aaarvee
aaarvee engineering consultants limited.
 (Formerly Aarvee Associates Architects Engineers & Consultants Private Limited)
 Registered Office Address: 9-2-5, Ravula Residency, Serangoon Colony Main Road, Hyderabad-500002; Telangana, India.
 Tel. : +91-40-4940550, 53771635; Fax : +91-40-4940527; email: sarvesh@aarvee.net, web@aarvee.com
 CMAA/142007/2009/PS/COE/0691

RG.No: AA/WCR/ELS/2616/MKN-3RD/P&P/105 SHEET NO : 105

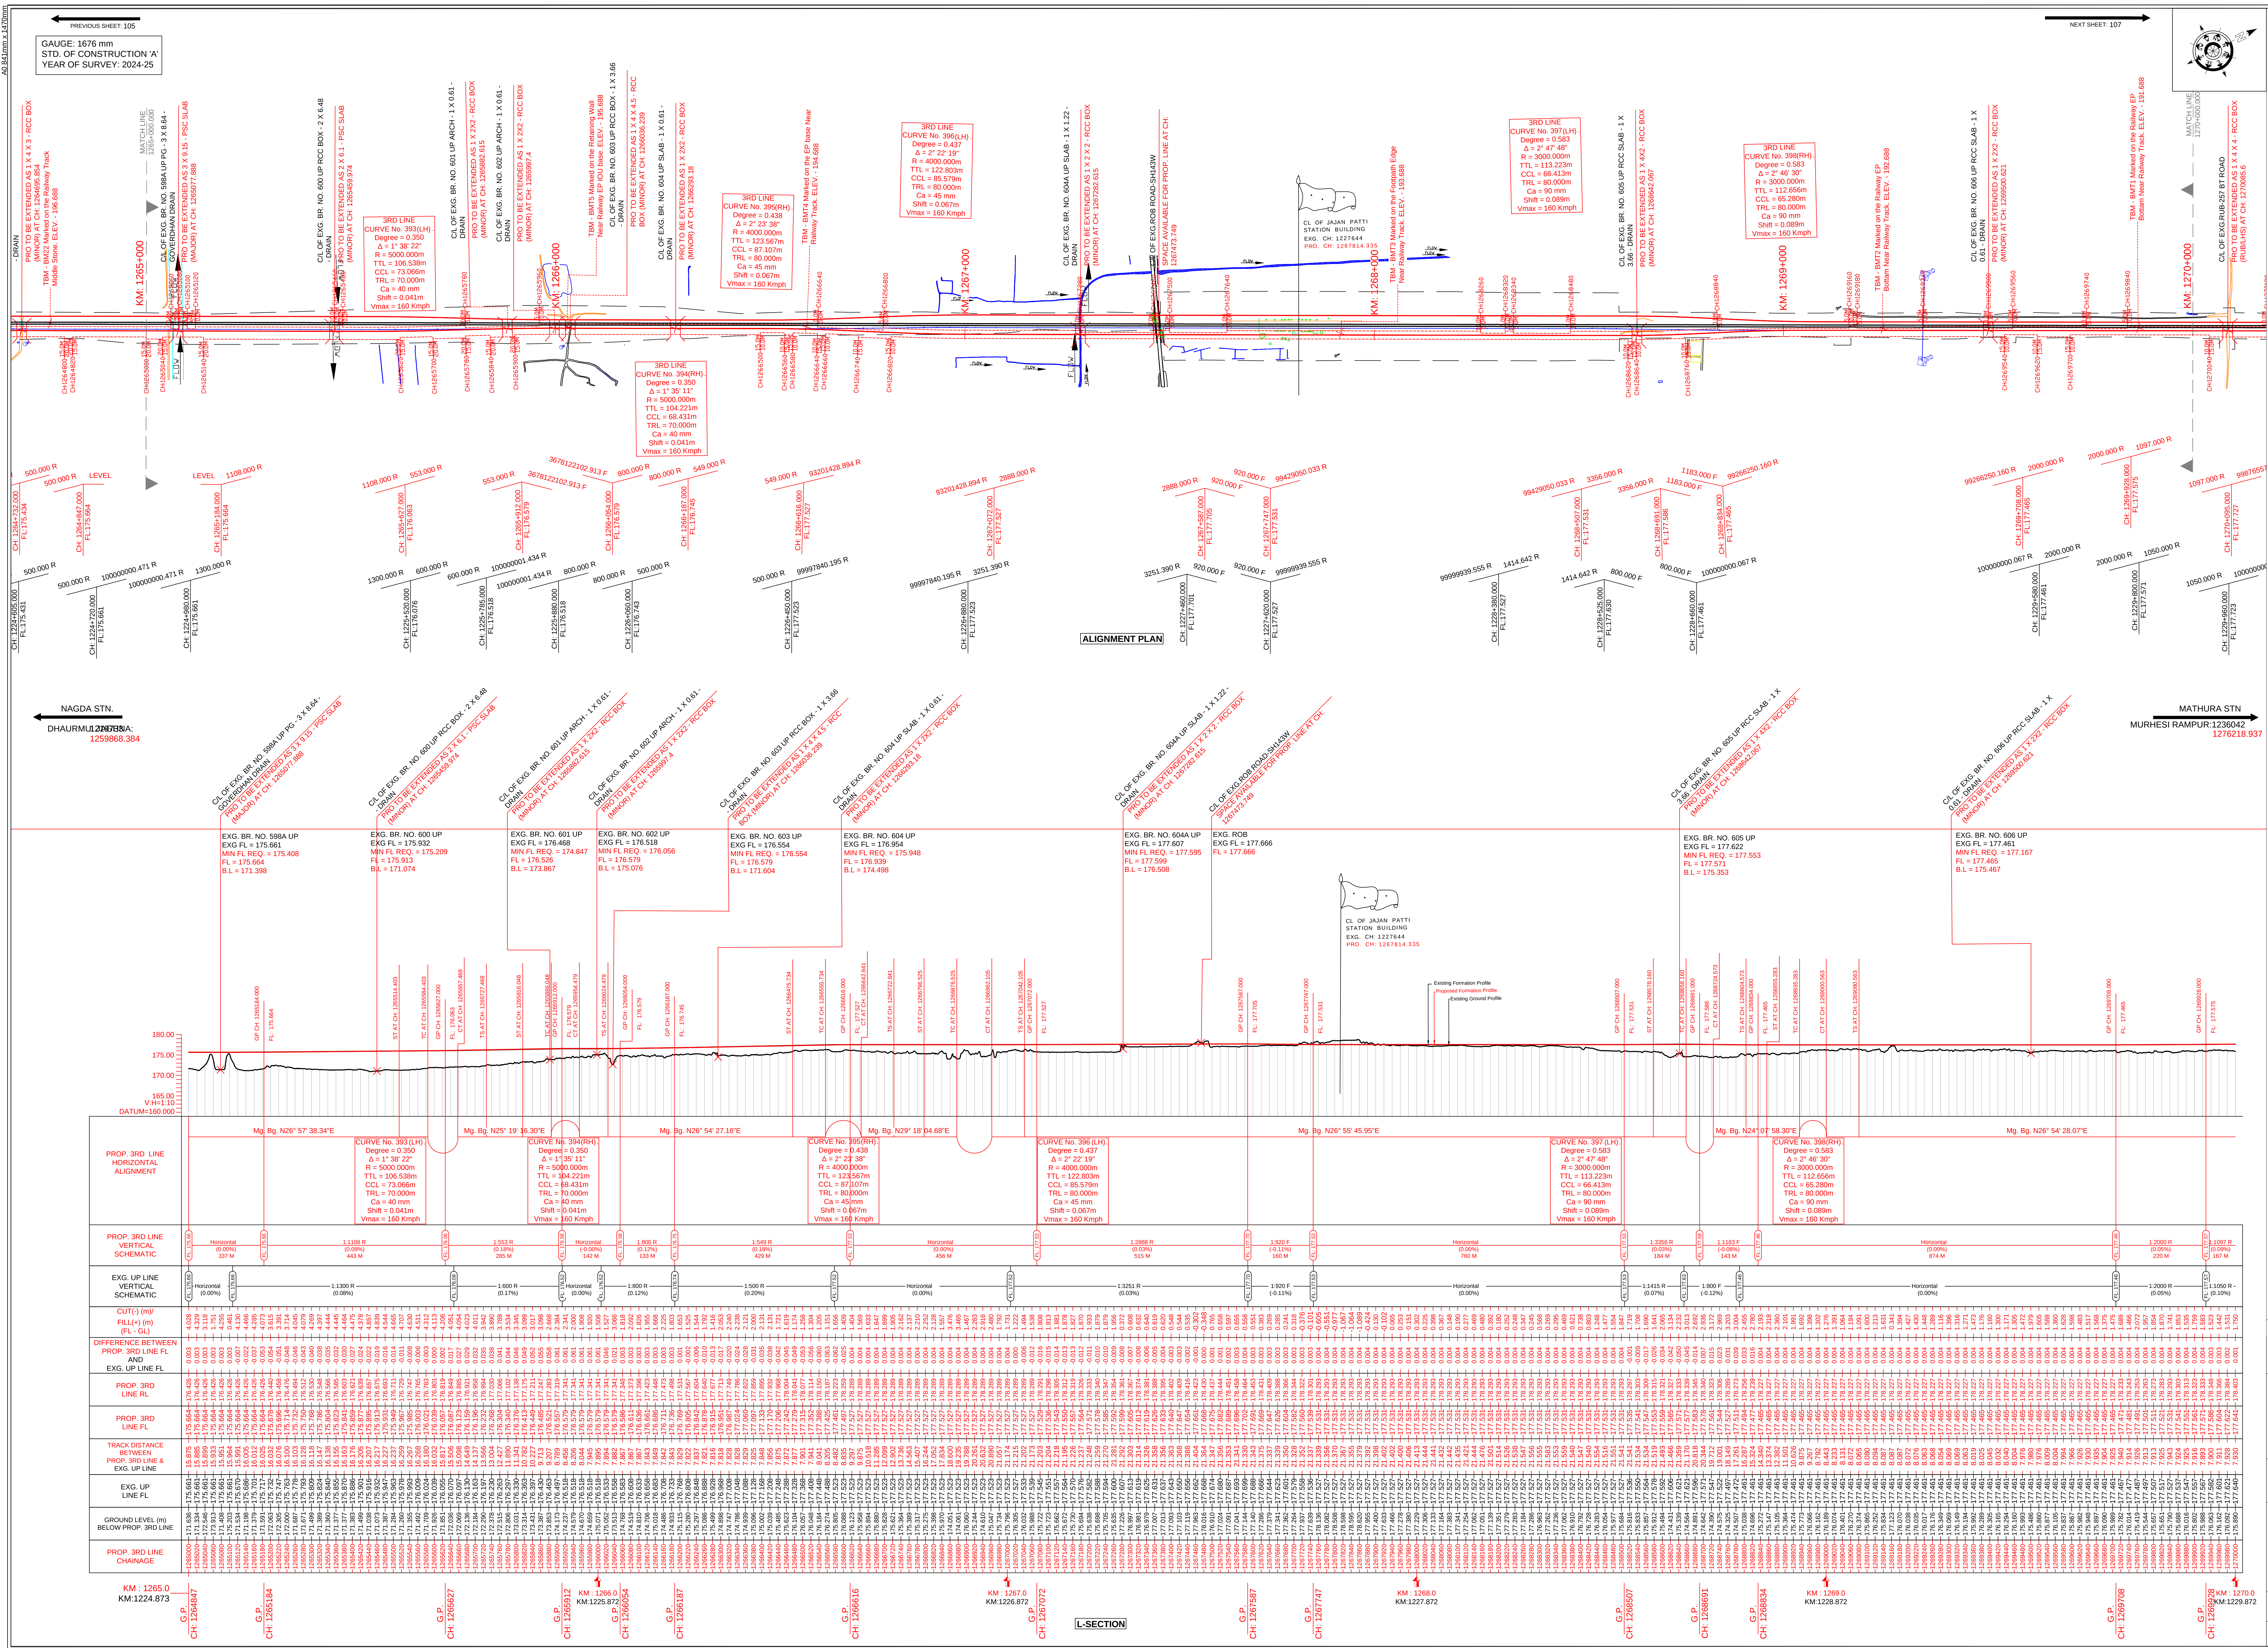

- NOTE:
1. ALL DIMENSIONS ARE IN METERS, UNLESS OTHERWISE SPECIFIED.
 2. EXISTING WORK SHOWN IN BLACK.
 3. PROPOSED WORK SHOWN IN RED.
 4. AS PER TERMS OF REFERENCE YARD GRADIENT HAVE BEEN EASED TO THE EXTENT POSSIBLE MAINTAINING GRADIENT AS 1 IN 150 (COMPENSATED).
 5. RAIL LEVEL SHOULD BE 762 MM ABOVE FORMATION LEVEL FOR TRACK STRUCTURE OF 60 KG NEW RAIL ON PSC WIDER SLEEPER (1660 NOS PER KM) WITH 350 MM BALLAST CUSHION.
 6. RULING GRADIENT OF THIS SECTION IS 1 IN 150.
 7. AS PER ENGINEERING CODE, VERTICAL CURVE WILL BE PROVIDED AT SITE WHERE ALGEBRAIC DIFFERENCE BETWEEN TWO GRADES IS EQUAL OR MORE THAN 4MM PER METER OR 0.4%.
 8. LAND TO BE ACQUIRED SHOWN IN DASHED RED.
 9. THE CHAINAGE AND KILOMETERS SHOWN ARE RECKONED FROM CENTER LINE OF SITE PLAN.
 10. THE SECTION IS DESIGNED FOR MAXIMUM SECTIONAL SPEED OF 160 KMPH.
 11. THE PROPOSED FORMATION AND BRIDGES IN THE SECTION IS DESIGNED FOR 25 T-2008 AXLE LOADING.

TBM DETAILS					
TBM ID	Chainage	Easting	Northing	MSL	Description
BMT5	1266027.959	753841.063	3026818.044	195.688	Marked on the Retaining Wall Near Railway EP ICU Side
BMT4	1266613.277	754106.261	3027339.966	194.688	Marked on the EP base Near Railway Track
BMT3	1267918.969	754709.272	3028497.77	193.688	Marked on the Footpath Edge Near Railway Track
BMT2	1269242.141	755295.539	3029683.763	192.688	Marked on the Railway EP Bottom Near Railway Track
BMT1	1269866.732	755576.188	3030241.755	191.688	Marked on the Railway EP Bottom Near Railway Track

LEGENDS:			
EXISTING RAILWAY TRACK		EXISTING ROW	
PROPOSED RAILWAY TRACK		METAL ROAD	
PROPOSED ROW		UN-METAL ROAD	
PRO. BRIDGES			
ELECTRIC LINES			
HT LINES			
WATER BODIES			
RAILWAY STRUCTURES			

<u>ABBREVIATIONS</u>			
R = Radius	PVI = Point of Vertical Intersection	L = Length	
Δ = Angle	TTP1 = Tangent to Transition Point-1	FL = Formation Level	
TRL = Transition Length	CTP1 = Curve Tangent Point-1	RL = Rail Level	
TL = Tangent Length	CTP2 = Curve Tangent Point-2	G = Gradient	
SL = Straight Line Length	TTP2 = Tangent to Transition Point-2		
CL = Curve Length	BVC = Beginning of Vertical Curve		
CCL = Circular Curve Length	EVC = End of Vertical Curve		
IP = Intersection Point	ERL = Existing Rail Level		
RTL = Road Top Level	BL = Bed Level		

REFERENCE DRAWINGS	
DRAWING TITLE	DRAWING No.
DRG.NO.DY.CE/C/KOTA	
H.Q. DRG. NO. - CPM/KOTA/E	
NAME OF THE OFFICER & DESIGNATION	SIGNATURE
(VIJAY PANDEY) CPM/WCR/KOTA	
(GAURAV MISHRA) DY.CE/C/KOTA	
(RAJESH YADAV) AXEN/KOTA	
(P.K. KANWA) SSE/W/C/KOTA	
(L.S. MEENA) JE/DRG/KOTA	

ISSUE RECORD					
1	01-07-2025	R0	SIVA THUTHA	RAMMOHAN	RAMAKRISHNA
No.	DATE	REV	PREPARED BY	CHECKED BY	APPROVED BY

CLIENT:  WEST CENTRAL RAILWAY
KOTA DIVISION

PROJECT : CONDUCTING FINAL LOCATION SURVEY (FLS) INCLUDING PREPARATION OF DPR, GEOTECHNICAL INVESTIGATION, SIGNALING WORK, ELECTRICAL WORKS AND OPERATING/TRAFFIC WORK FOR CONSTRUCTION OF ELECTRIFIED NEW LINE/DOUBLING/THIRD LINE/4TH LINE. FLY OVER WORK/BYPASS LINE ETC.



TITLE : DETAILED PLAN AND L SECTION MATHURA-NAGDA -3RD LINE
1265+000.000 TO 1270+000.000

CONSULTANT :

 **aarvee**
aarvee engineering consultants limited.

(Formerly Aarvee Engineering & Consultants Private Limited)
Registered Office Address: 9/51 Ravula Residency, Srinagar Colony, Main Road Hyderabad-500082 Telangana, India.
Tel: +91-40-6848348, 22776303 Fax: +91-40-22776377 Email: aaarvee@aarvee.net, info.aarvee.com
CIN:U70203TG2007PLC046491

DRG.No: AA/WCR/FLS/2616/MKN-3RD/P&P/106	SHEET NO : 106
SCALE : HOR : 1:5000 . VER : 1:500	DATE : 01-07-2025

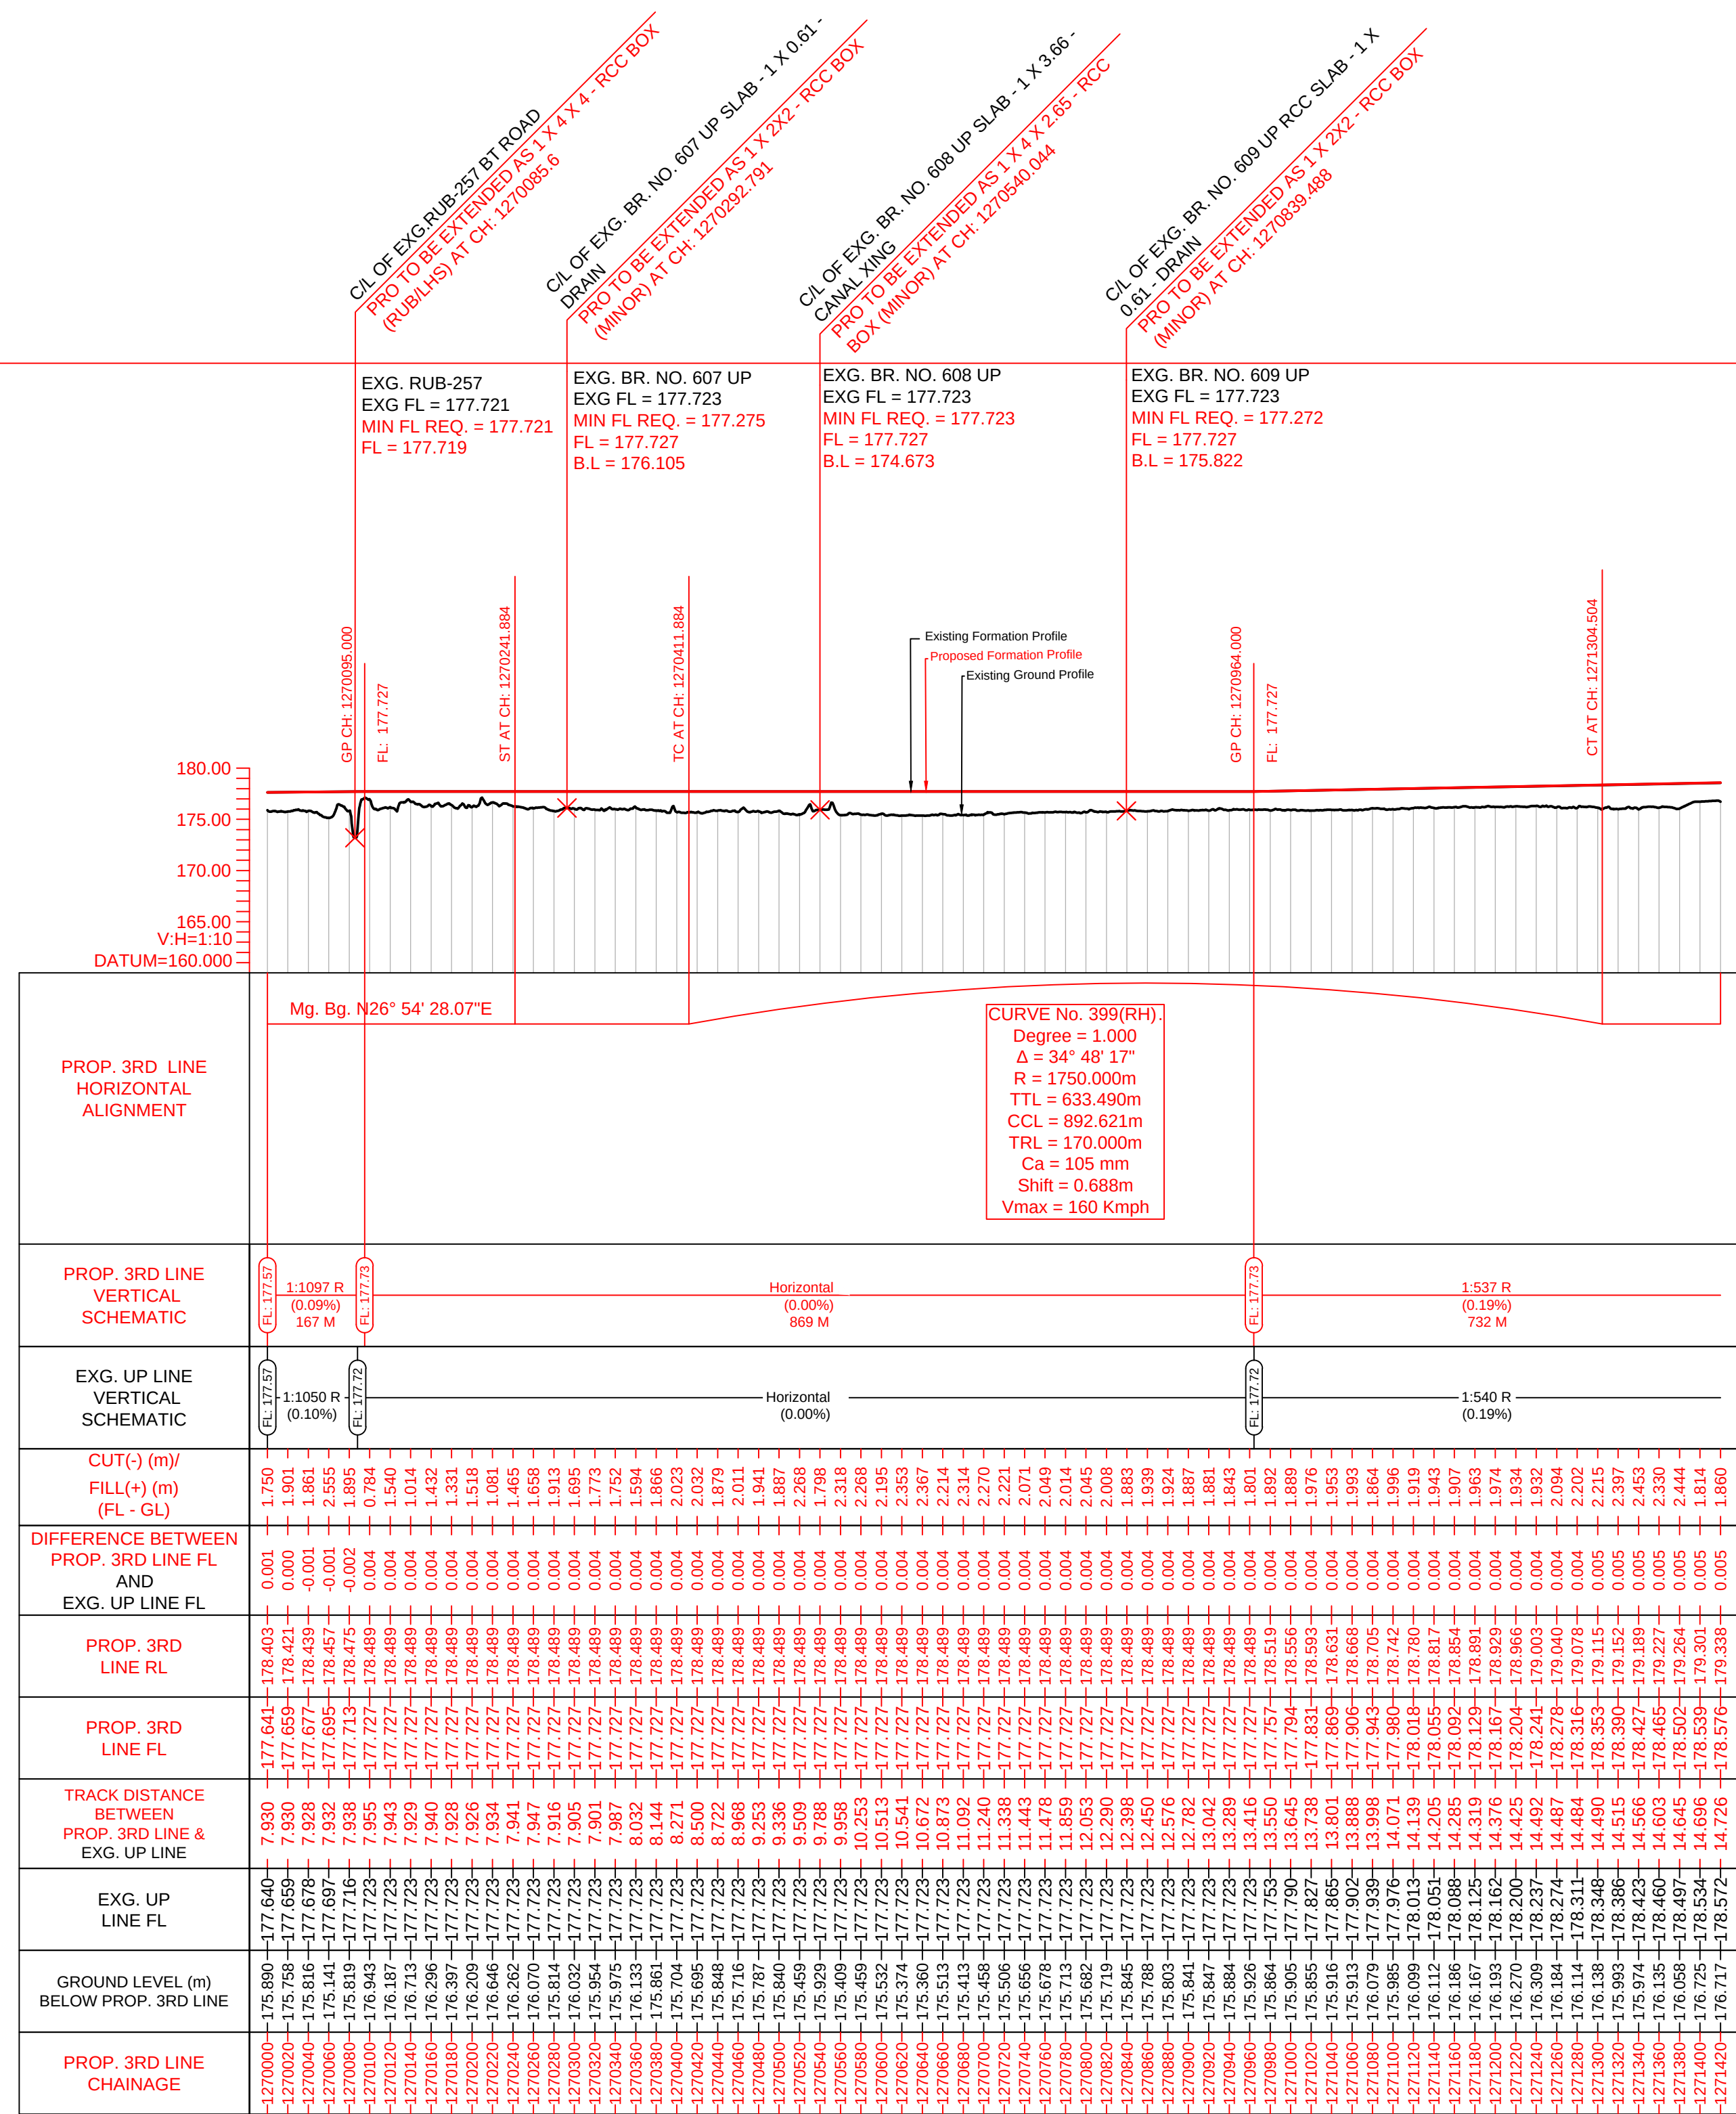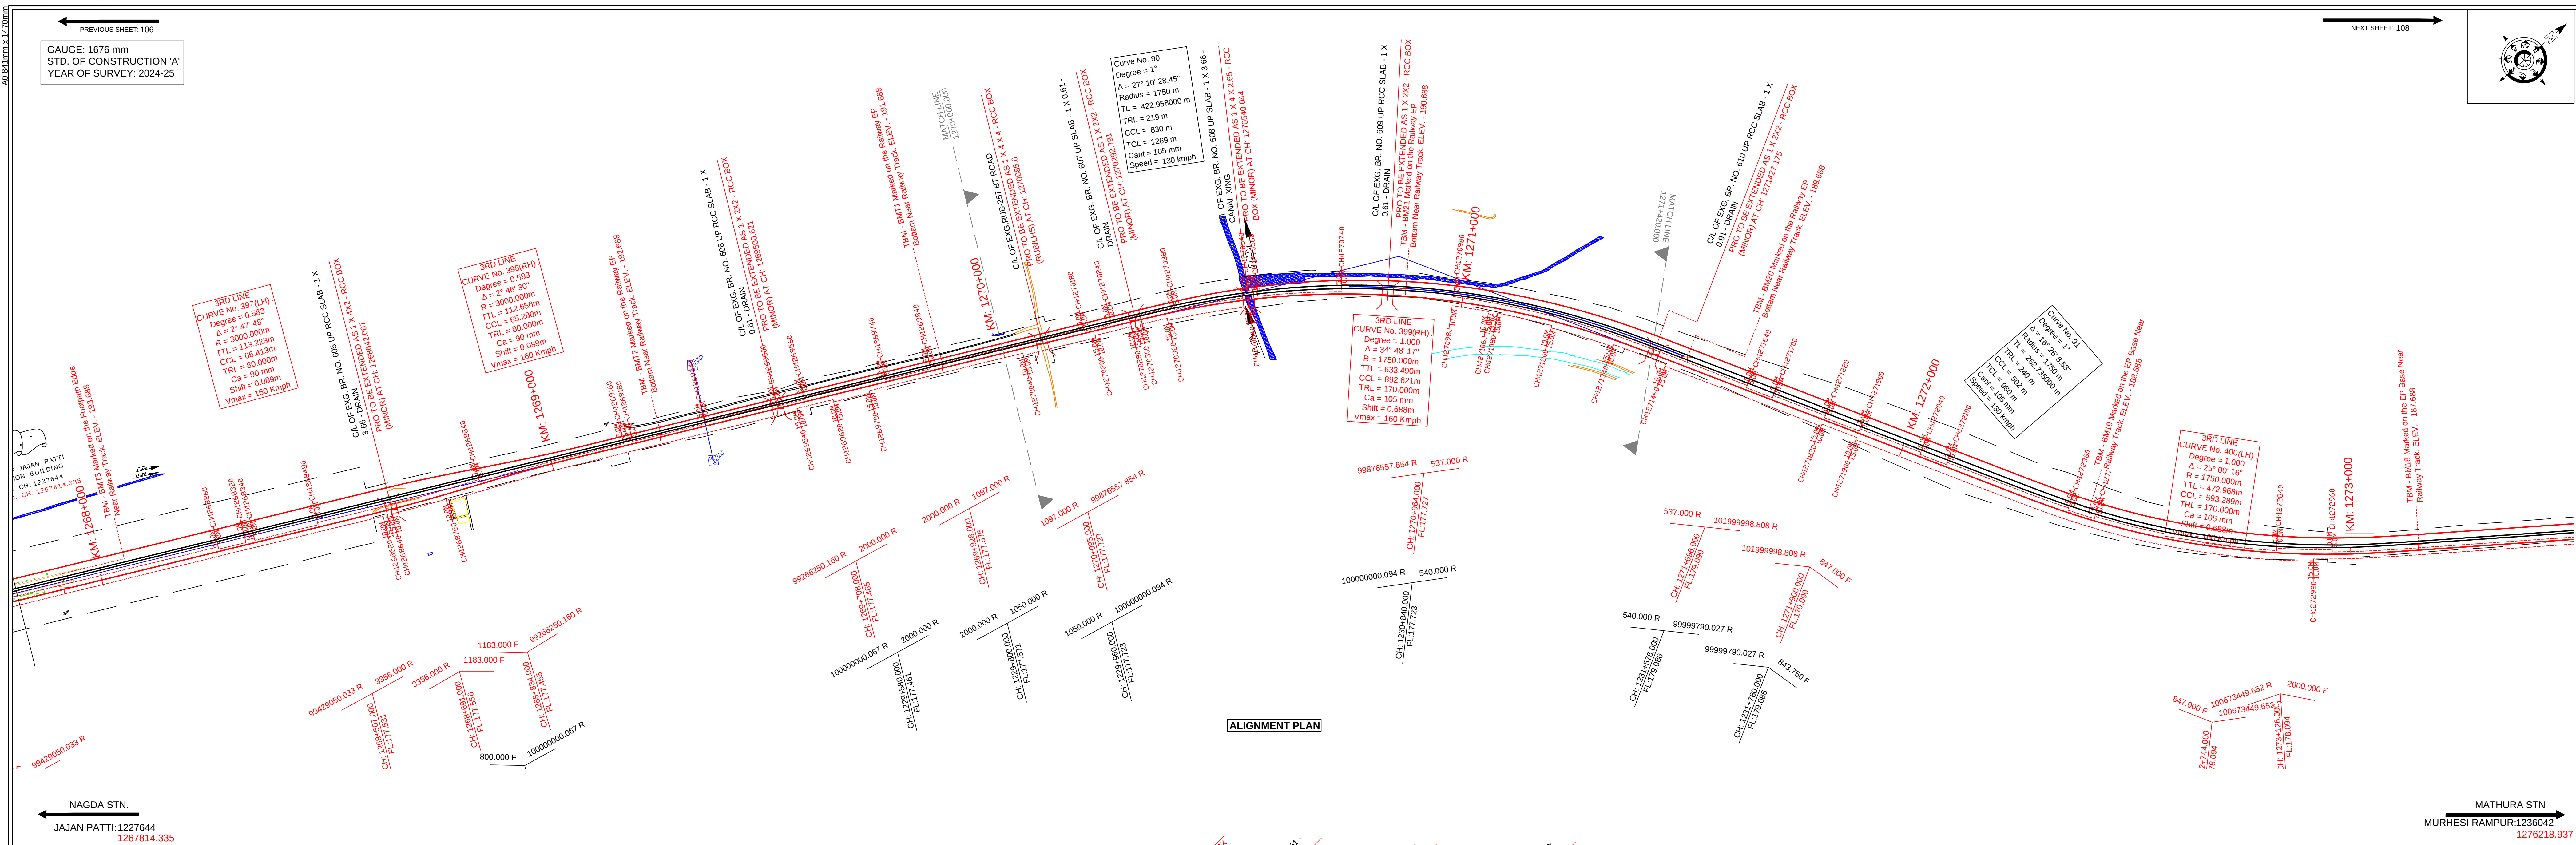

KM : 1270.0
KM:1229.872
G.P.
CH: 1269928

L-SECTION

G.P.
CH: 1270964
— KM: 1271.0
KM: 1230.876

KM : 1271.4
KM:1231.289

- NOTE:
1. ALL DIMENSIONS ARE IN METERS, UNLESS OTHERWISE SPECIFIED.
 2. EXISTING WORK SHOWN IN BLACK.
 3. PROPOSED WORK SHOWN IN RED.
 4. AS PER TERMS OF REFERENCE YARD GRADIENT HAVE BEEN EASED TO THE EXTENT POSSIBLE MAINTAINING GRADIENT AS 1 IN 150 (COMPENSATED).
 5. RAIL LEVEL SHOULD BE 762 MM ABOVE FORMATION LEVEL FOR CONCRETE STRUCTURE AND 100 MM ABOVE RAIL ON PSG WIDER SLEEPER (1680 NOS PER KM) WITH 350 MM BALLAST CUSHION.
 6. RULING GRADIENT OF THIS SECTION IS 1 IN 150.
 7. AS PER ENGINEERING CODE, VERTICAL CURVE WILL BE PROVIDED AT SITE WHERE ALGEBRAIC DIFFERENCE BETWEEN TWO GRADES IS EQUAL OR MORE THAN 4MM PER METER OR 0.4%.
 8. LAND TO BE ACQUIRED SHOWN IN DASHED RED.
 9. THE CHAINAGE AND KILOMETERS SHOWN ARE RECKONED FROM GENTK JNR OF ST AS 0.00
 10. THE SECTION IS DESIGNED FOR MAXIMUM SECTIONAL SPEED OF 160 KMPH.
 11. THE PROPOSED FORMATION AND BRIDGES IN THE SECTION IS DESIGNED FOR 25 T-2008 AXLE LOADING.

TBM DETAILS					
TBM ID	Chainage	Easting	Northing	MSL	Description
BM21	1270877.307	756101.507	3031103.683	190.688	Marked on the Railway EP Bottom Near Railway Track.

LEGENDS:

EXISTING RAILWAY TRACK		EXISTING ROW	
PROPOSED RAILWAY TRACK		METAL ROAD	
PROPOSED ROW		UN-METAL ROAD	
PRO. BRIDGES			
ELECTRIC LINES			
HT LINES			
WATER BODIES			
RAILWAY STRUCTURES			

ABBREVIATIONS

R	= Radius	PVI	= Point of Vertical Intersection	L	= Length
Δ	= Angle	PTP1	= Tangent to Transition Point-1	FL	= Formation Level
TRL	= Transition Length	CTP1	= Curve Tangent Point-1	RL	= Rail Level
TL	= Tangent Length	CTP2	= Curve Tangent Point-2	G	= Gradient
SL	= Straight Line Length	TPP2	= Tangent to Transition Point-2		
CL	= Curve Length	BVC	= Beginning of Vertical Curve		
CCL	= Circular Curve Length	EV	= End of Vertical Curve		
IP	= Intersection Point	ERL	= Existing Rail Level		
RTL	= Road Top Level	BL	= Bed Level		

REFERENCE DRAWINGS	
DRAWING TITLE	DRAWING No.
DRG.NO.DY.CE(C)/KOTA	
H.Q. DRG. NO.- CPM/KOTA/E	
NAME OF THE OFFICER & DESIGNATION	SIGNATURE
(VIJAY PANDEY) CPMWCR/KOTA	
(GAURAV MISHRA) DY.CE/C/KOTA	
(RAJESH YADAV) AXEN/KOTA	
(P.K. KANWA) SSE/W/KOTA	
(L.S. MEENA) JE/DRG/KOTA	

ISSUE RECORD					
1	01-07-2025	R0	SIVA THUTA	RAMMOHAN	RAMAKRISHNA
No.	DATE	REV	PREPARED BY	CHECKED BY	APPROVED BY

CLIENT:  WEST CENTRAL RAILWAY
KOTA DIVISION

PROJECT : CONDUCTING FINAL LOCATION SURVEY (FLS) INCLUDING PREPARATION OF DPR, GEOTECHNICAL INVESTIGATION, SIGNALING WORK, ELECTRICAL WORKS AND OPERATING/TRAFFIC WORK FOR CONSTRUCTION OF ELECTRIFIED NEW LINE/DOUBLING/THIRD LINE/4TH LINE. FLY OVER WORK/BYPASS LINE ETC.

TITLE : DETAILED PLAN AND L SECTION MATHURA-NAGDA -3RD LINE
1270+000.000 TO 1271+420.000

CONSULTANT :

 **aarvee**
aarvee engineering consultants limited.
(Formerly Aarvee Associates Architects Engineers & Consultants Private Limited)
Registered Office Address: 8-5, Ravula Road, Rongireddy, Sangareddy, Chiknayakanahalli Road, Hyderabad-500085, Telangana, India.
Tel : +91-40-4943456, 23737033. Fax : +91-40-23735027, email: aarvee@aarvee.net, web@aarvee.com
CIN:U72900TG2006PLC048491

DRG.No: AA/WCR/FLS/2616/MKN-3RD/P&P/107 SHEET NO : 107

SCALE : HOR : 1:5000 , VER : 1:500	DATE : 01-07-2025
------------------------------------	-------------------